


# Hotellet vid Götaplatsen




Gestaltning av en byggnad som både samspelar med det gamla och bidrar med något nytt i en karaktärsfull urban miljö.

# Situation

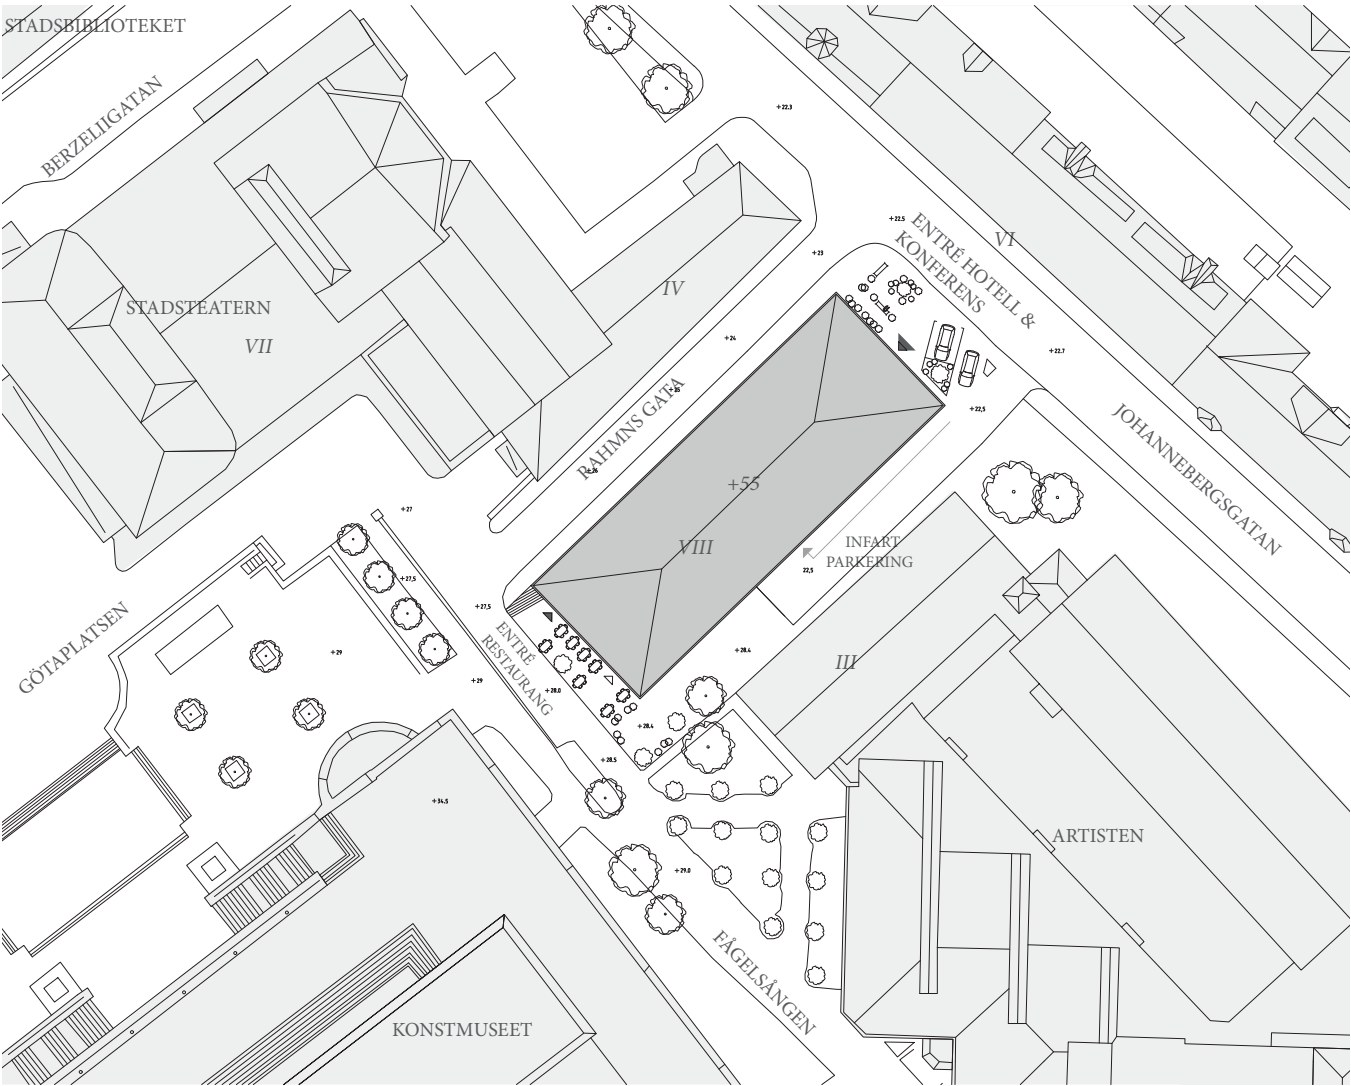


SITUATIONSPLAN

# Fasader

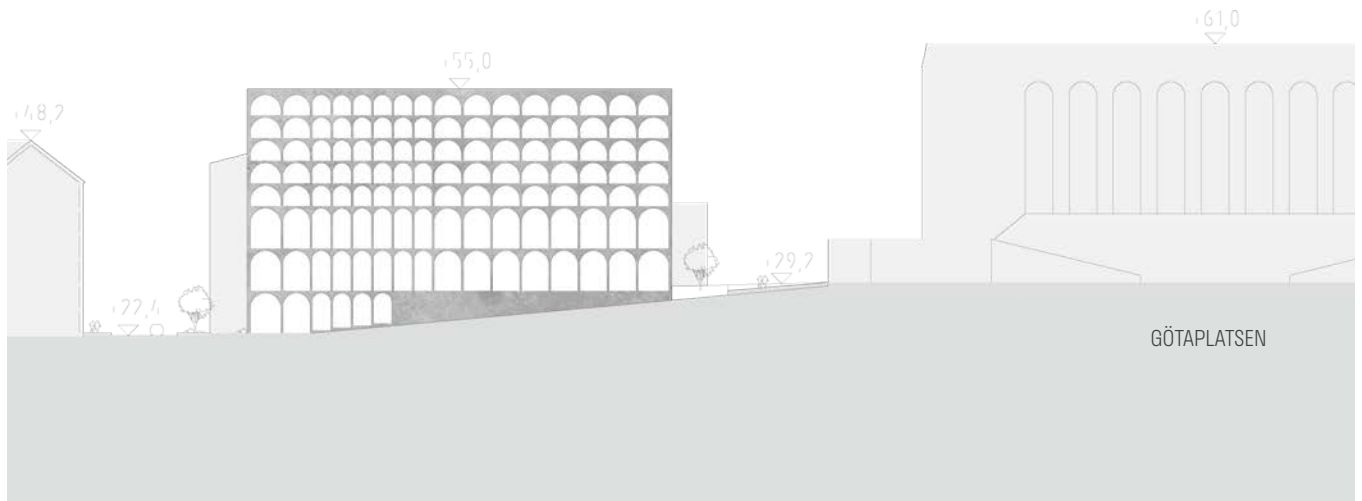

**FASAD FRÅN NORDVÄST (MOT RAHMNS GATA)**

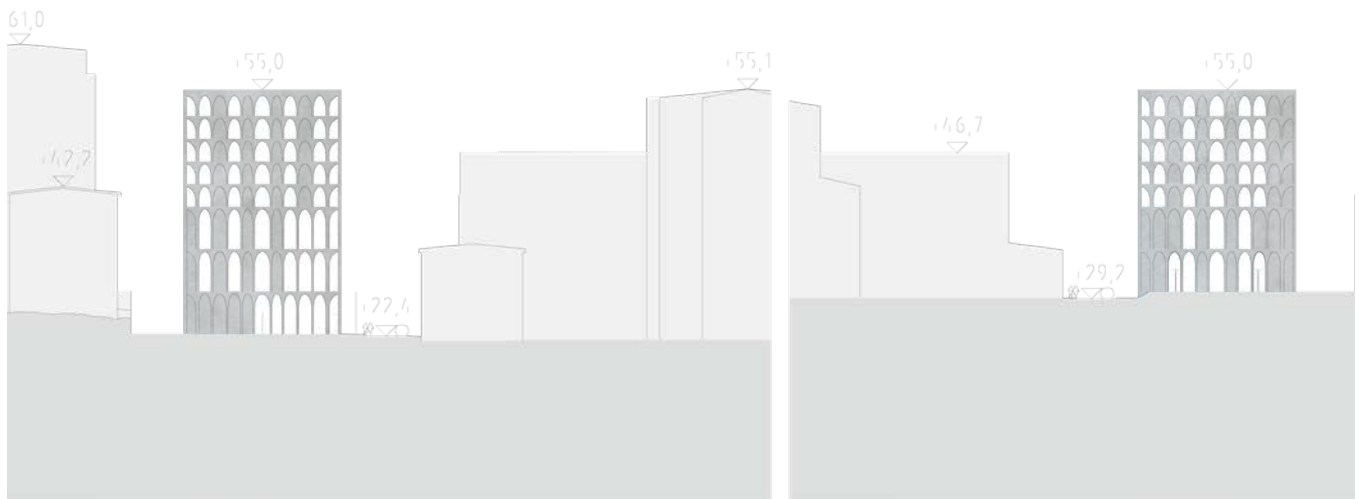


**FASAD FRÅN NORDÖST (MOT JOHANNEBERGSGATAN)**


**FASAD FRÅN SYDVÄST (MOT GÖTAPLATSSEN)**

Fasaden är inspirerad av konstmuseets  
fasad med valv, i ett asymmetriskt mönster  
som ges utifrån planens indelning.




# Plan 1

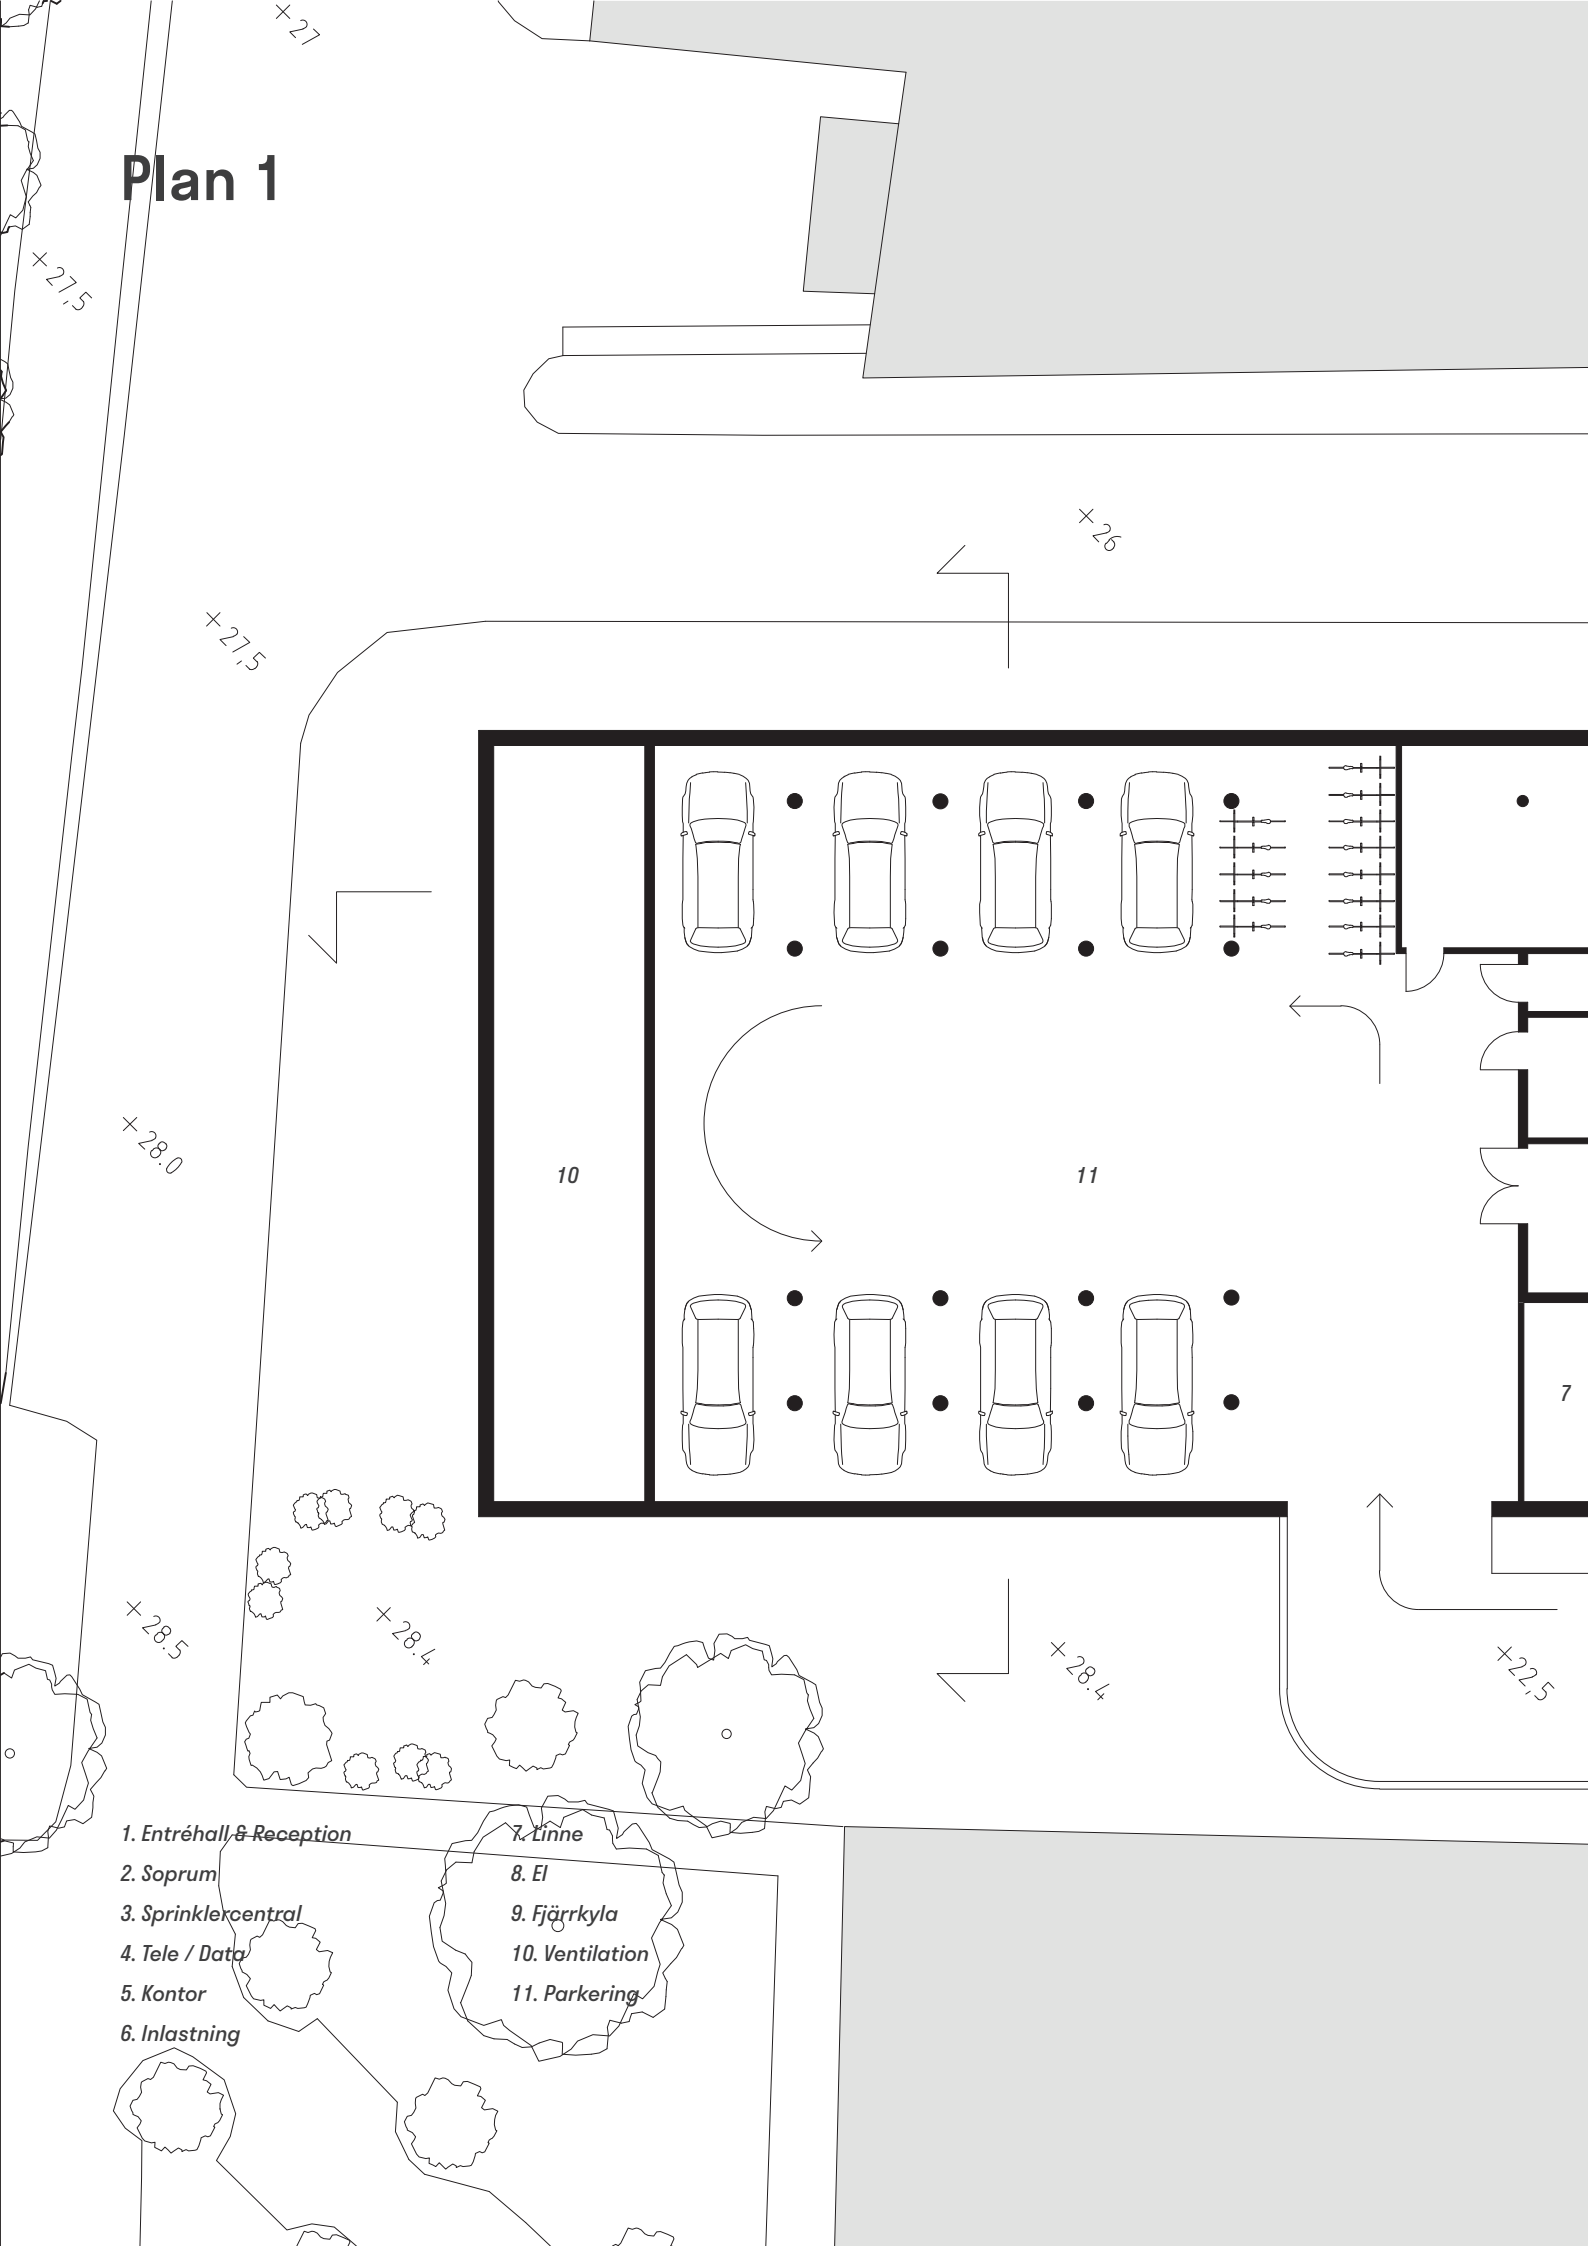


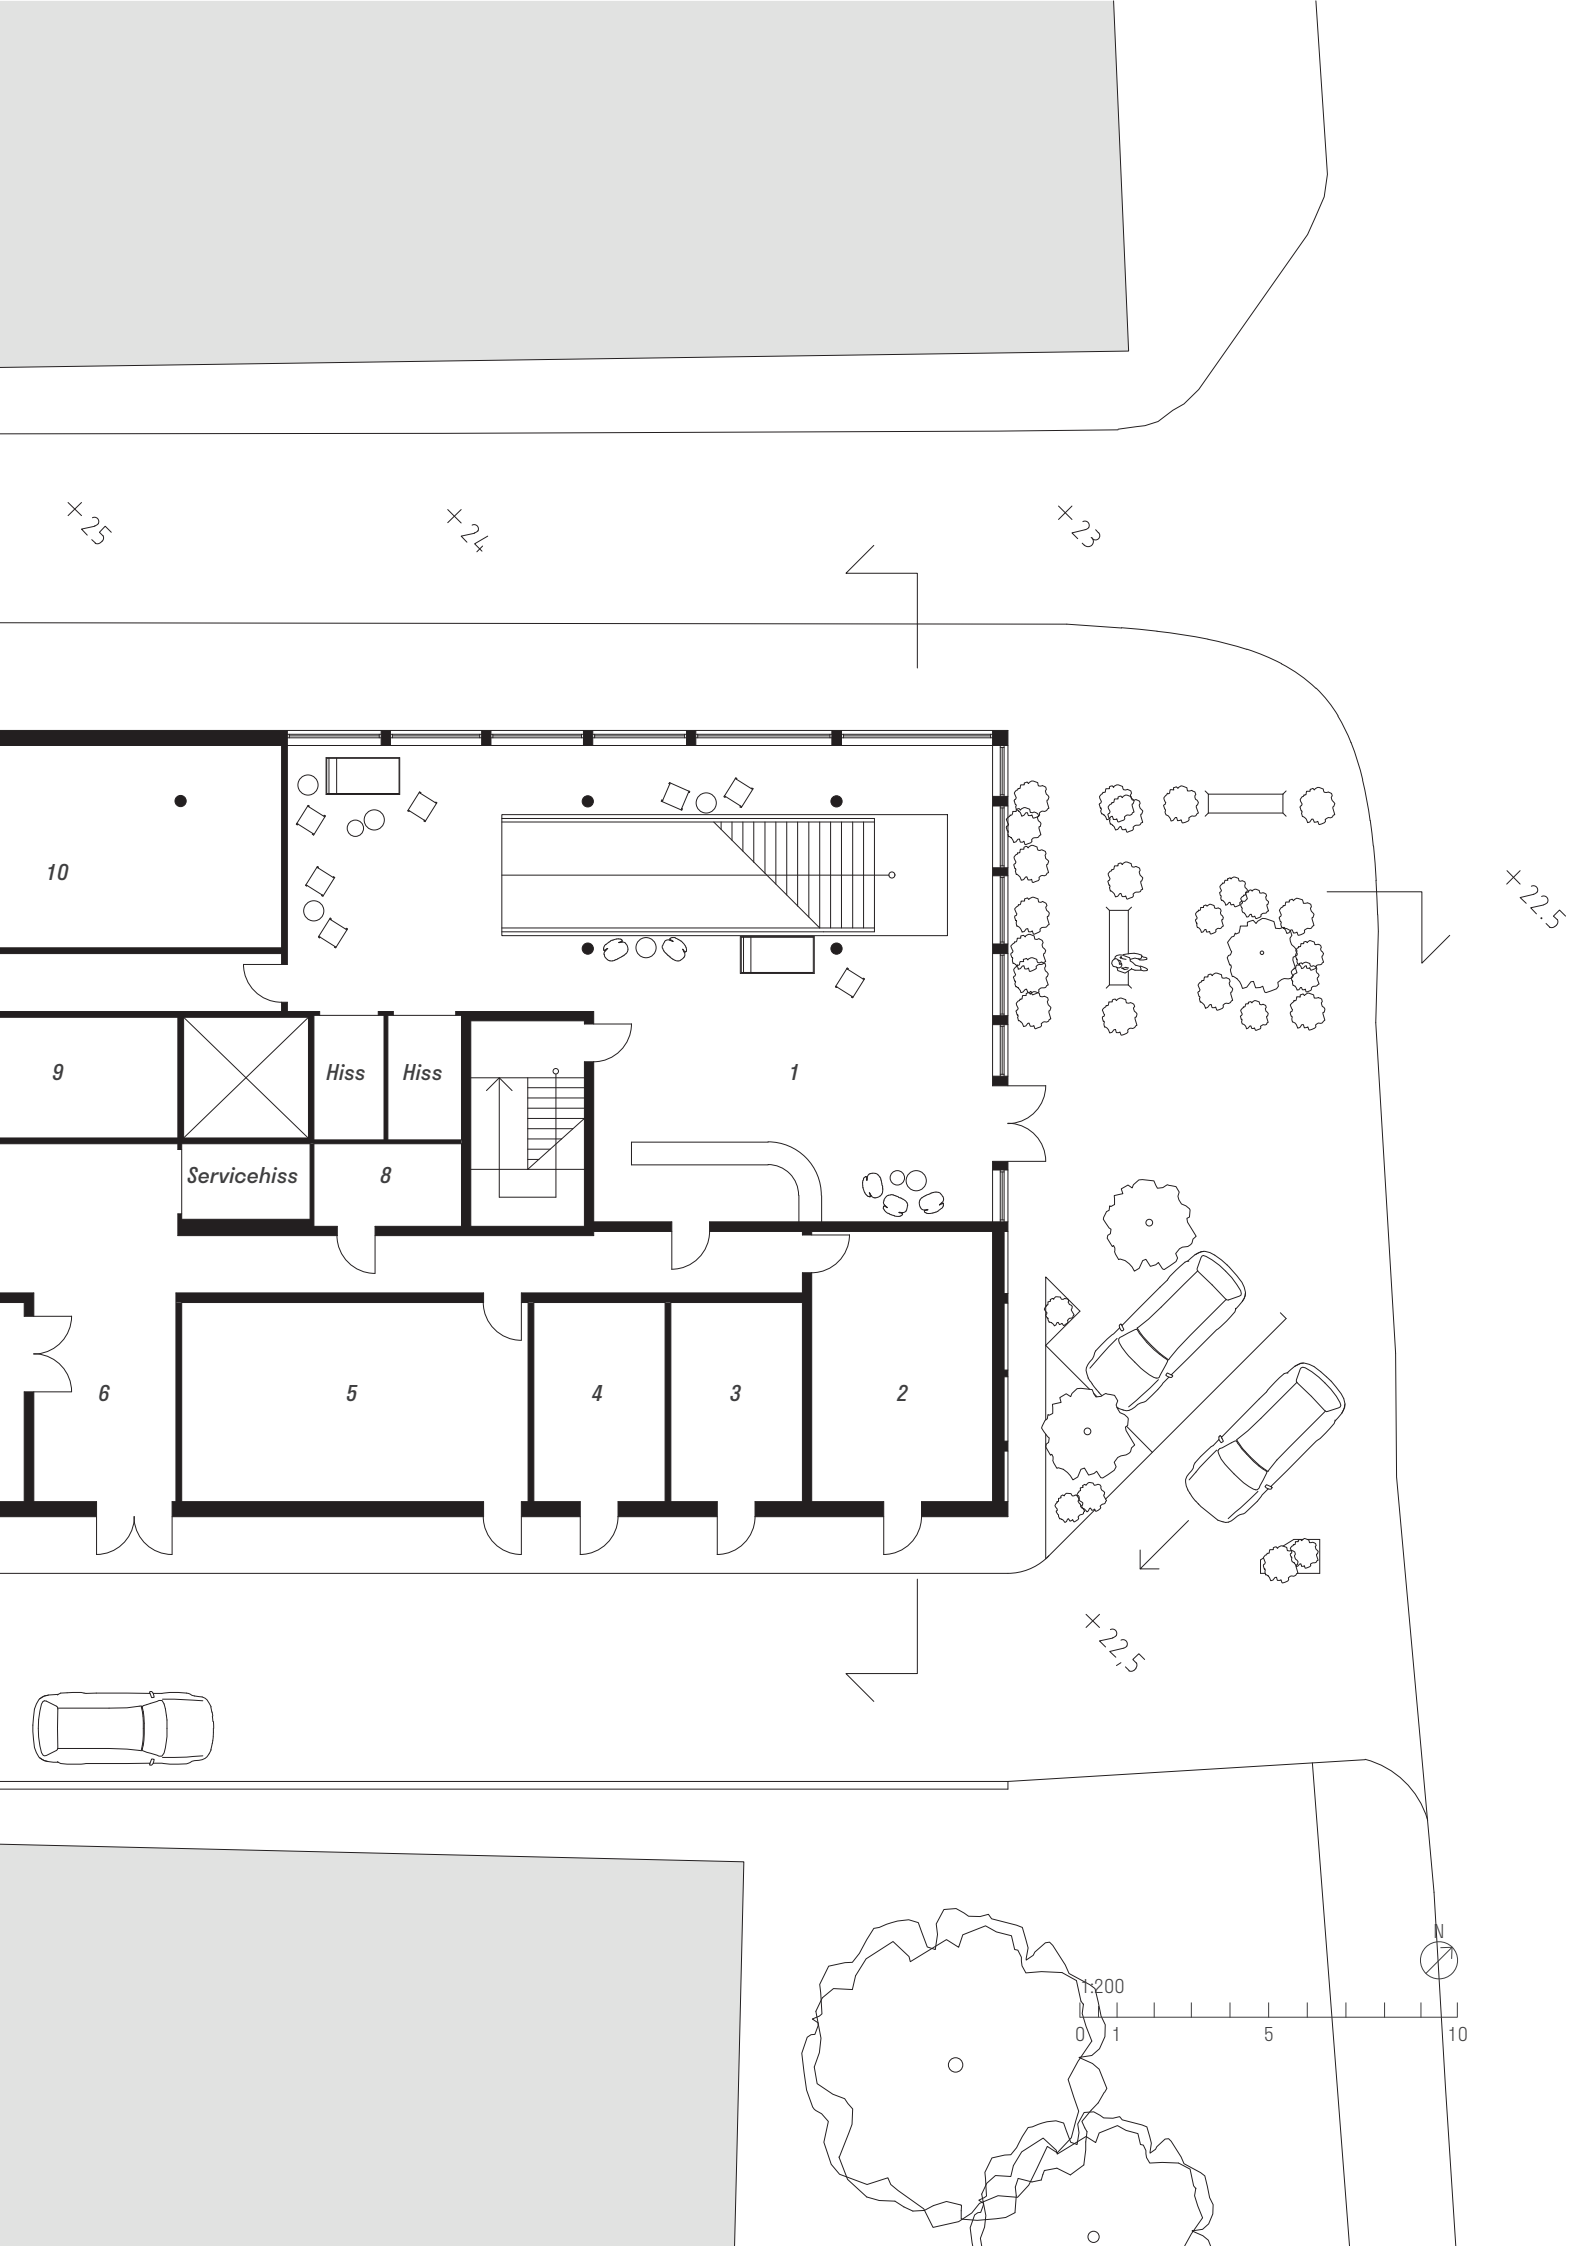

## Plan 2

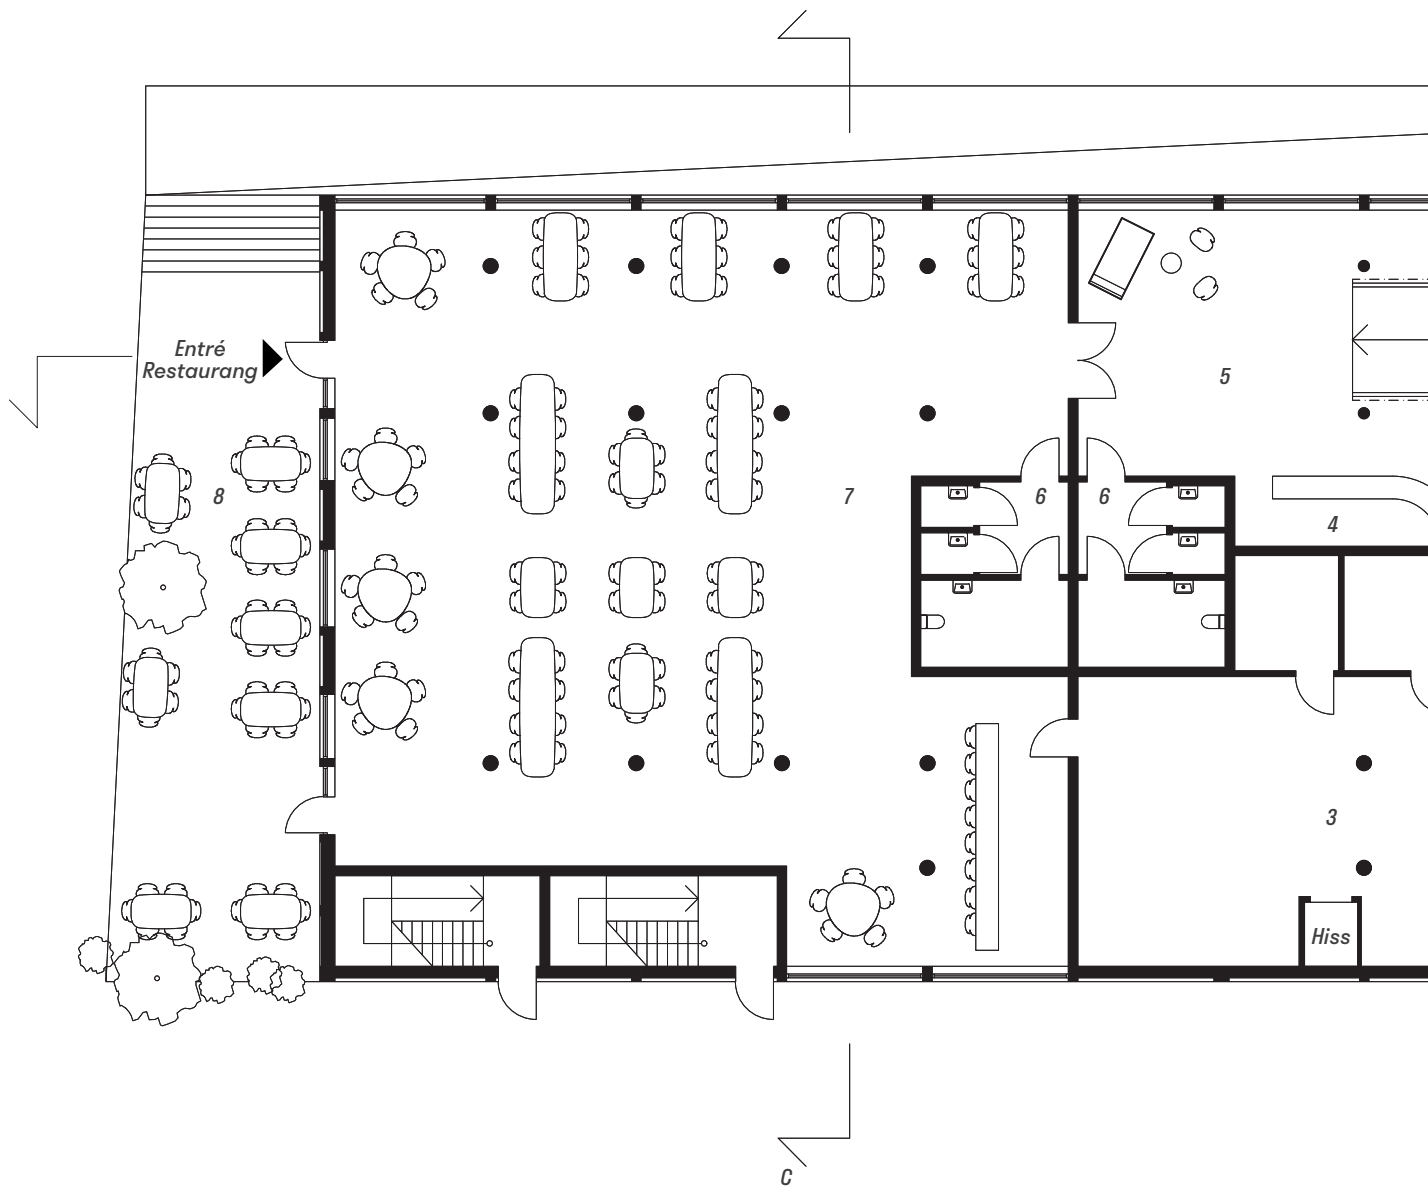


- |                        |                 |
|------------------------|-----------------|
| 1. Mötesrum 30P        | 6. WC           |
| 2. Mötesrum 10P        | 7. Restaurang   |
| 3. Kök                 | 8. Uteservering |
| 4. Reception konferens | 9. Förråd       |
| 5. Pausyta             |                 |

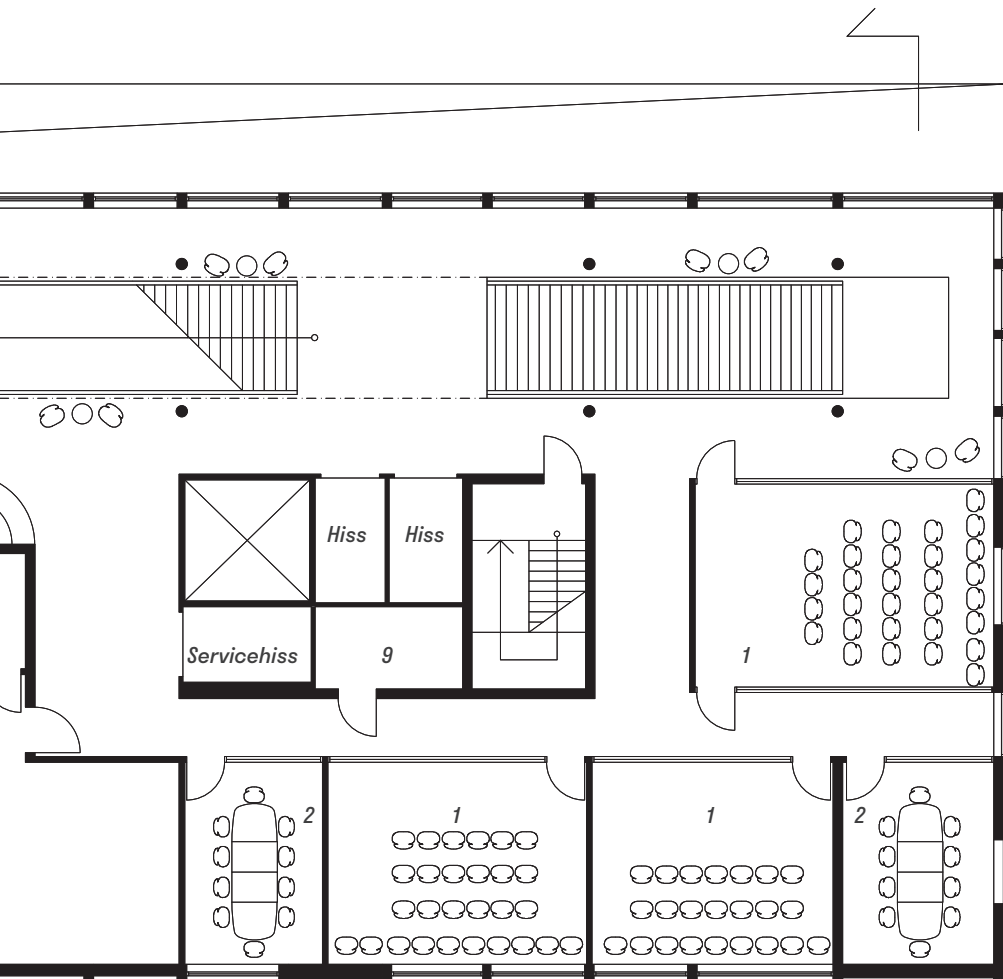


A

B

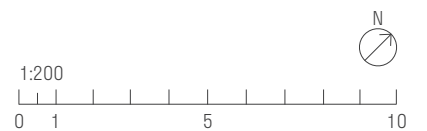


# Plan 3

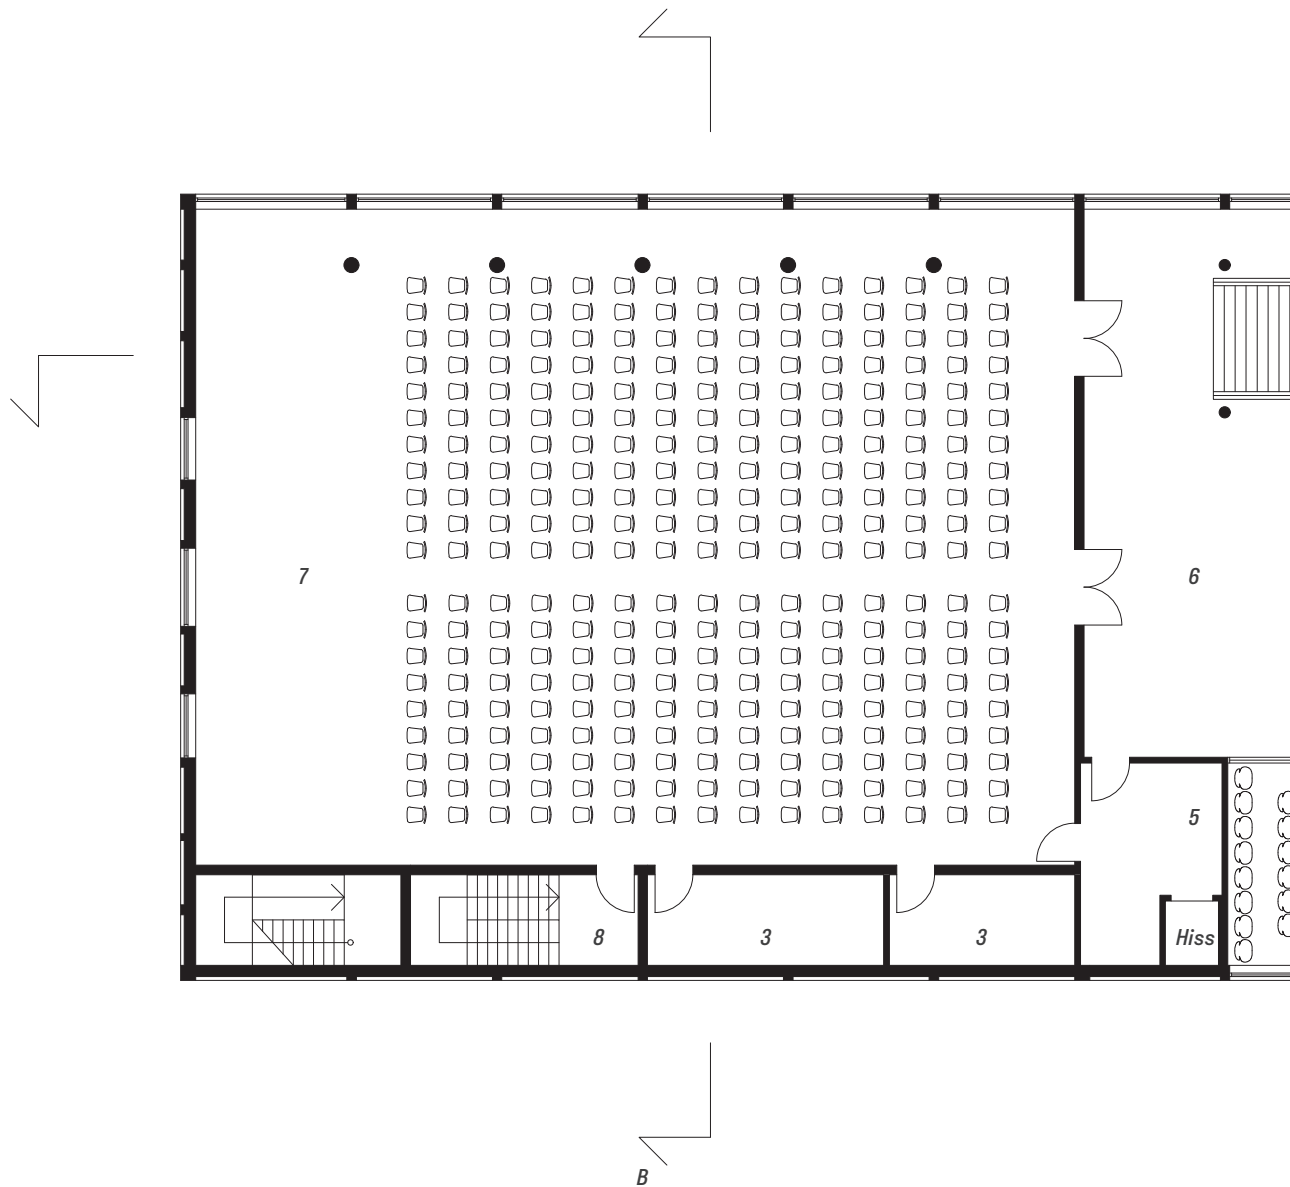

- 1. Mötesrum 20P
- 2. Mötesrum 10P
- 3. Förråd
- 4. WC


- 5. Serveringsrum
- 6. Pausyta
- 7. Samlingssal, 272 platser
- 8. Nödutgång



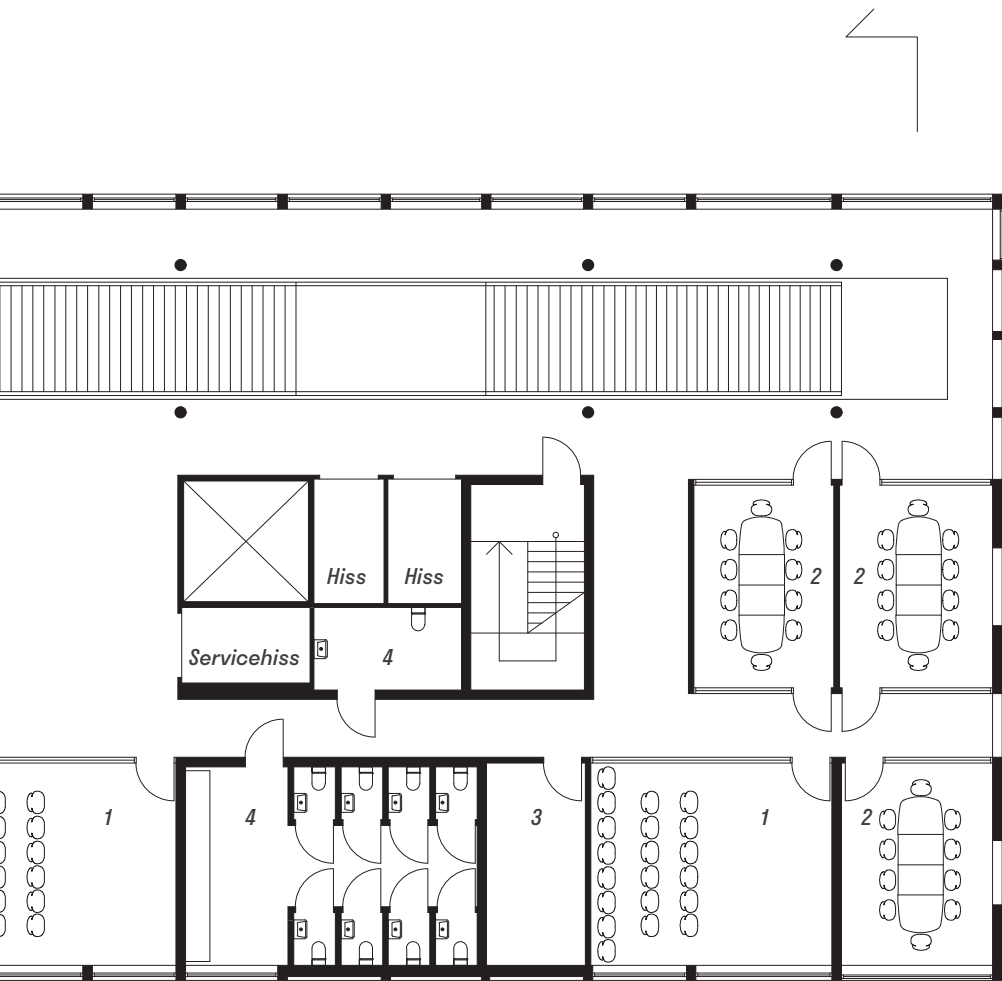


A




C

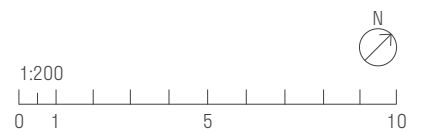

# Plan 4—8

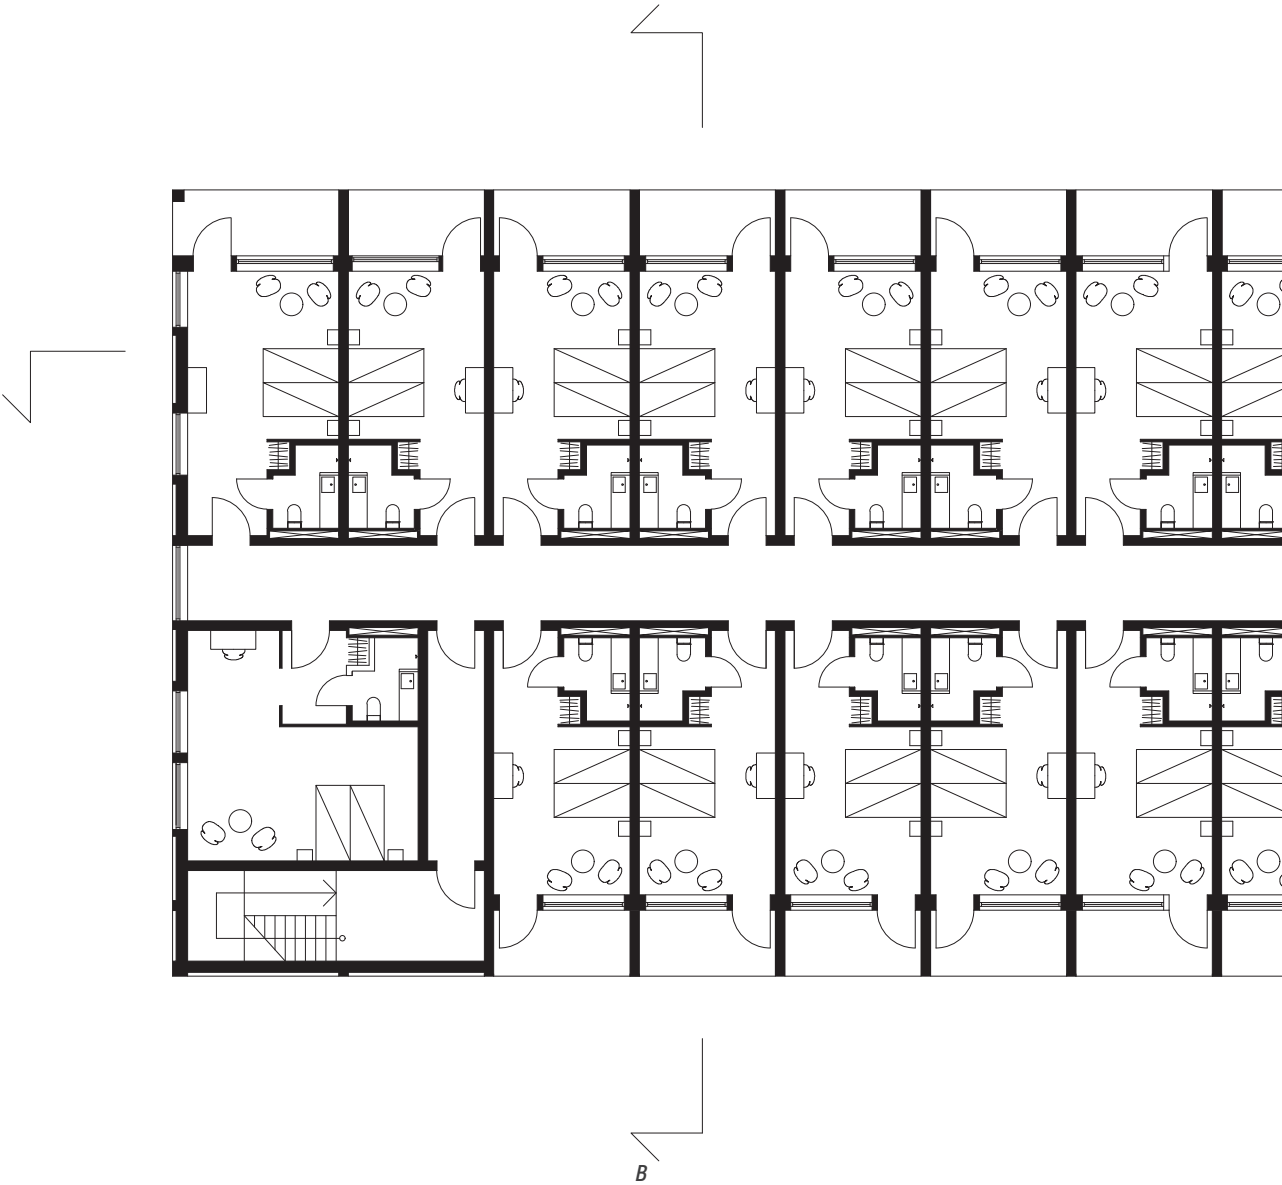


15 st rum Standard  
8 st rum Superior

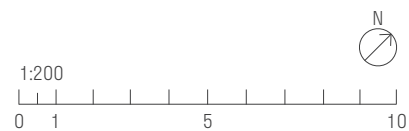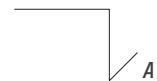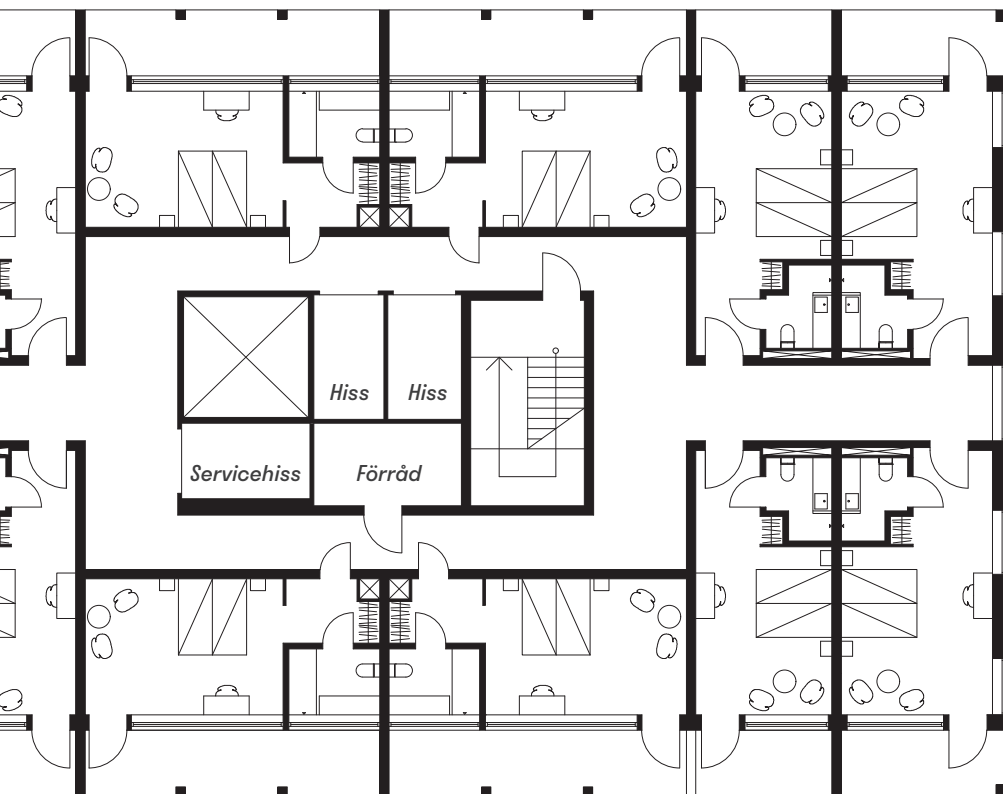


# Detalj B1

SEKTION MELLAN VÅNINGAR VID HOTELLRUM.  
GRÄNS MELLAN RUM, BALKONG, "YTTRE FASAD".

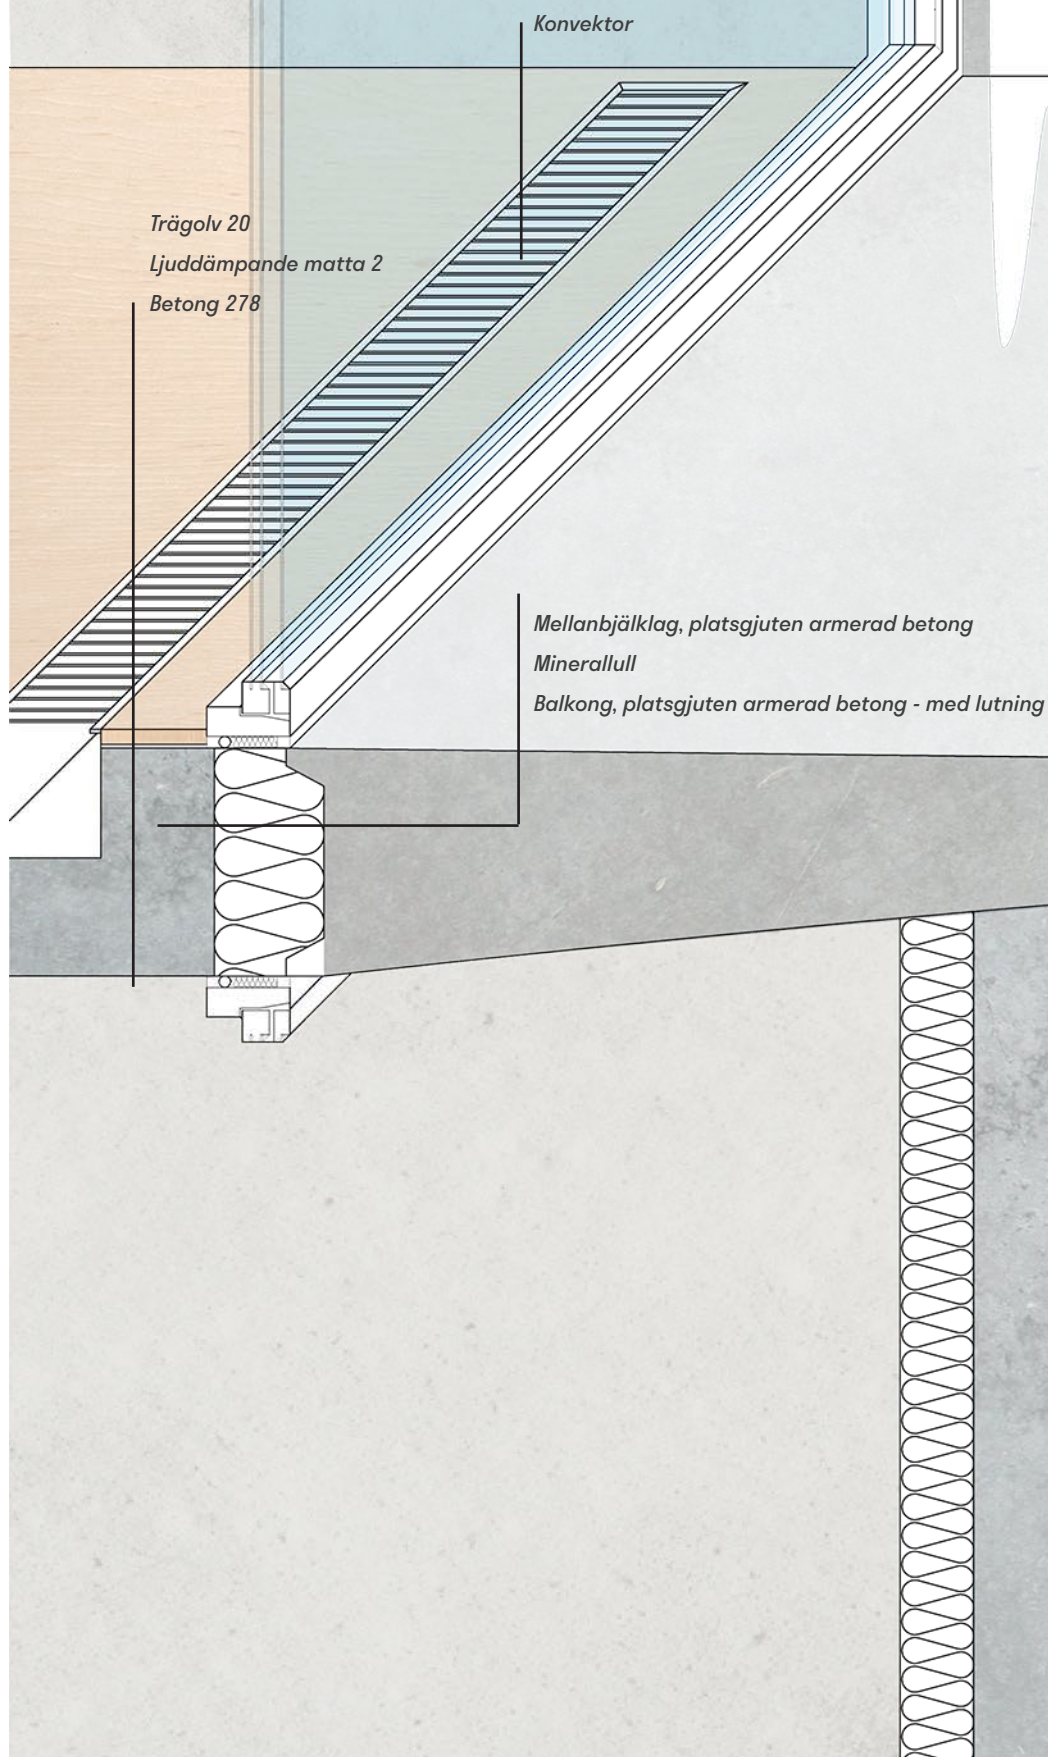



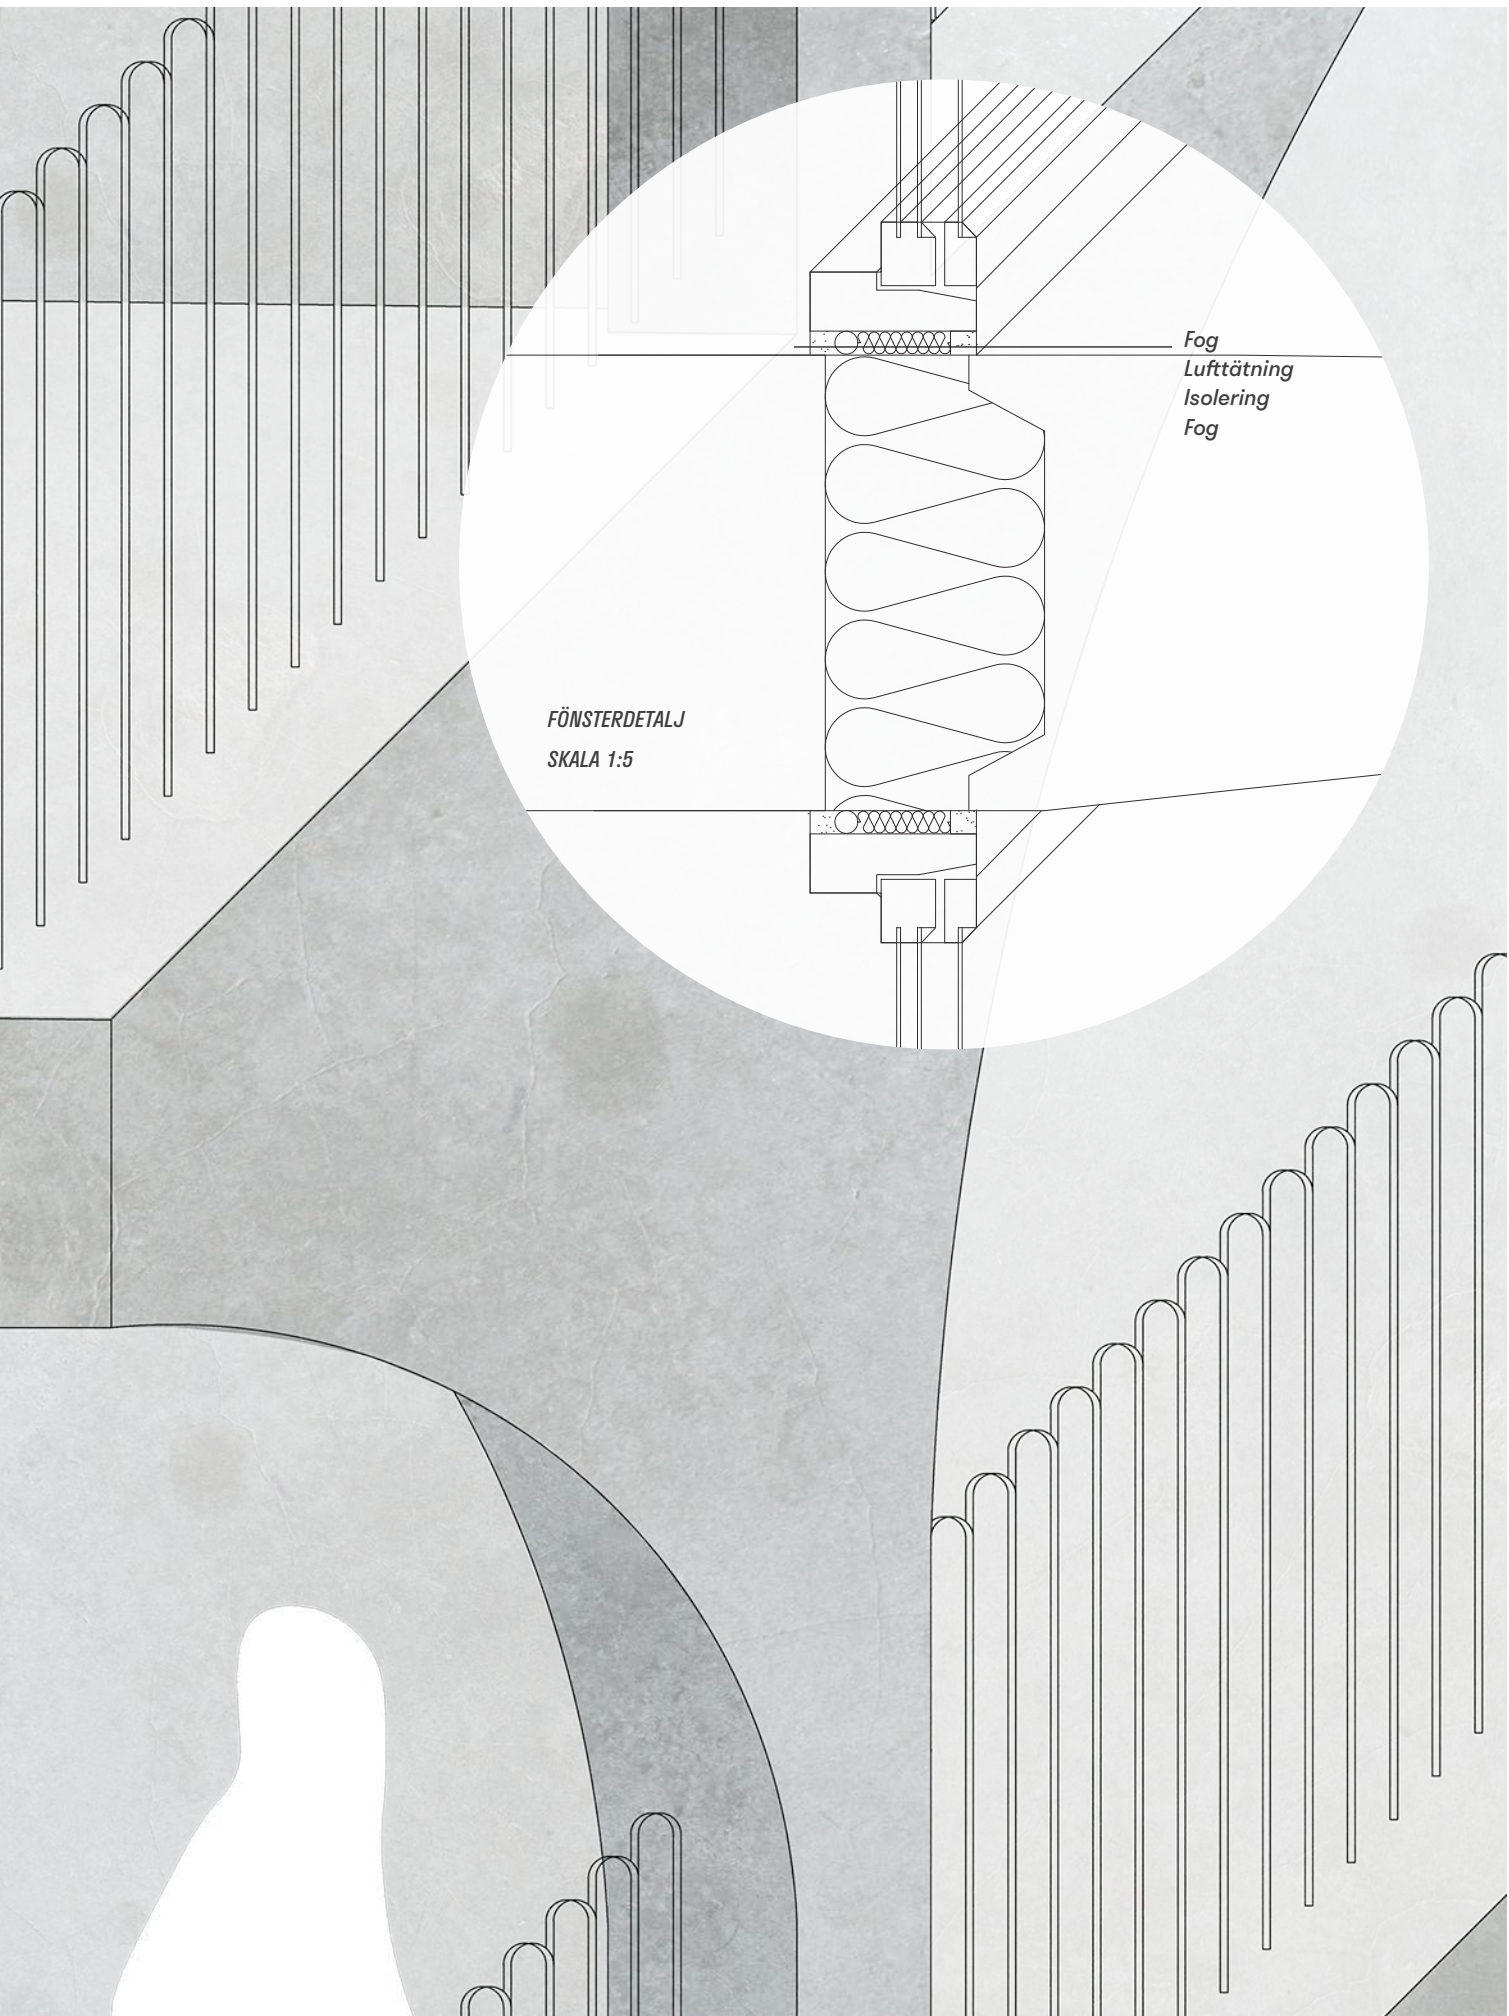

FÖNSTERDETALJ  
SKALA 1:5

Fog  
Lufttätning  
Isolering  
Fog