

Kandidatprojekt

MAJNABBE



Uppgiften — att utforma en stadsdel
och byggnader utifrån koncepten
robusthet och flexibilitet

Utveckla Majnabbe!

Området är en speciell plats med närhet till Älven, med utsikt mot havet, Älvsborgsbron och Eriksbergskranen. Tillåt hela Göteborg åtkomst till platsen! Det ska vara bekvämt att röra sig i området även för de som inte bor där—en inbjudande och tillåtande miljö skapas. Promenaden knyter ihop Röda Sten med gång- och cykelväg till centrala Göteborg. Platsen blir sammankopplande, men också en attraktion i sig.

*Brobänkarna
rekonstrueras som
rekreationsyta,
anknytning till områdets
historia.*

● VÄGBANA

● CYKELBANA

Färjeläge







Byggnad som hyser
kulturverksamhet,
replokaler mm.
bevaras.

SEKTION

SITUATIONSPLAN
1:3000

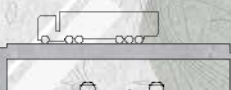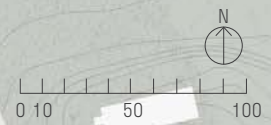

SEKTION
1:1000




Husen och stadsrummet



EXEMPEL HUVUDGATA

SKALA 1: 500

Huvudgatan är 15,8 m bred. Solsidan har en bred trottoar, med plats för träd, förträdgårdar, cykel- och bilparkering, uteservering och utställningsyta för butiker. På andra sidan bilvägen finns en dubbelfilig cykelbana och en gångbana.

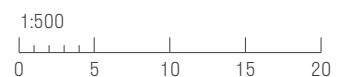





SEKTION GENOM HUS VID KAJ

SKALA 1:200

I det här utsnittet syns relation mellan hus, publik plats och vatten. Huset har sin skyddade entré, vid denna del av gatan kan även andra gränsfunktioner förläggas, som dels hör till de som verkar i huset, dels de som passerar. Efter detta en trädplantering, promenadstråk och en sittplats ner mot vattnet.

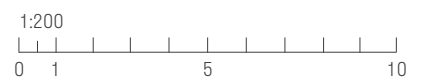

Gatuplan

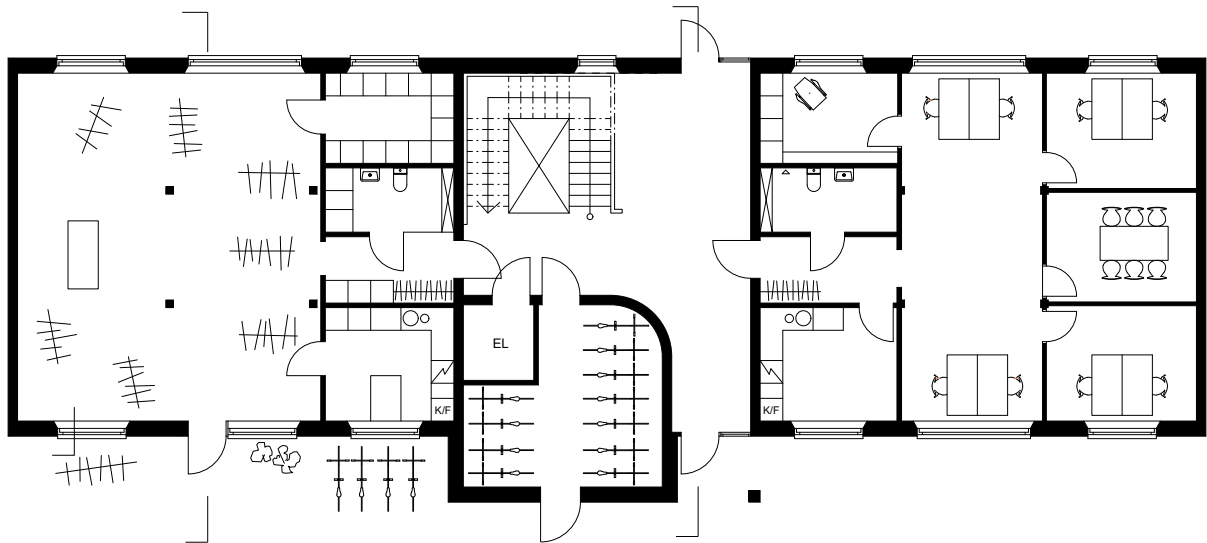


Plan 0, princip alt. 1 — Affärslokal och kontor

Mot Gata

Vid gränsen mellan hus och gata är på de flesta platser yta förberedd för att inredas med till exempel förträdgårdar, sittplatser, cykelparkering, uteservering eller utställningsyta för verksamheter.

Entré

Entré till huset sker under ett skyddande tak. Gård nås genom entréhallen.

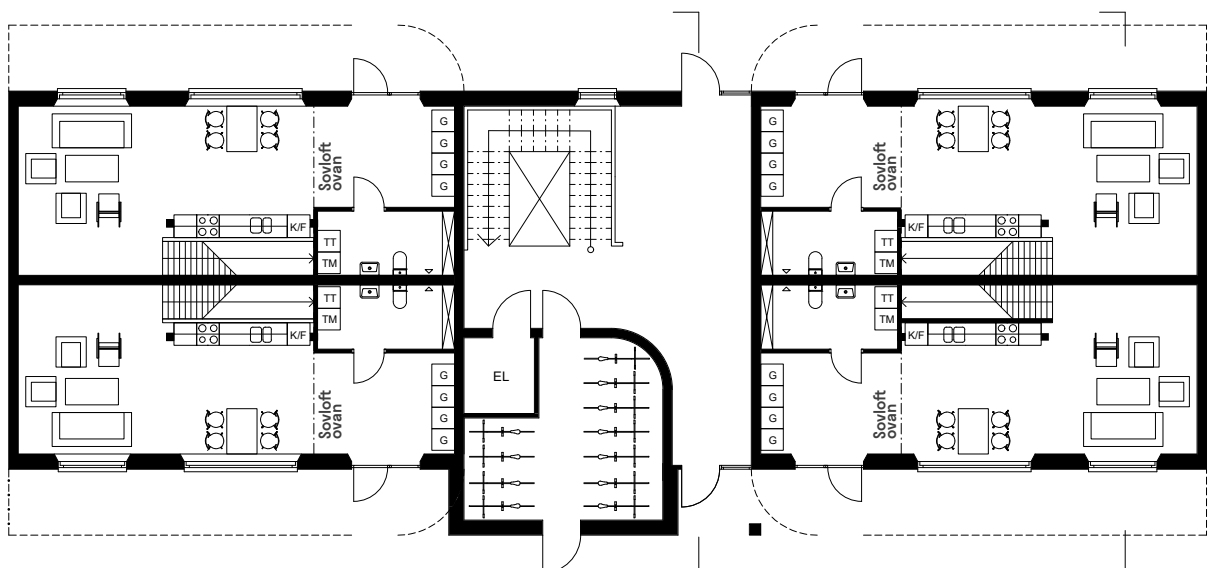


Plan 0, princip alt. 2 — Bostäder

Bostad

I vissa lägen kan det vara möjligt att ha bostäder även på markplan, här visas ett exempel på förslag till plan. Med en högre våningshöjd finns utrymme för ett sovloft.

Normalplan

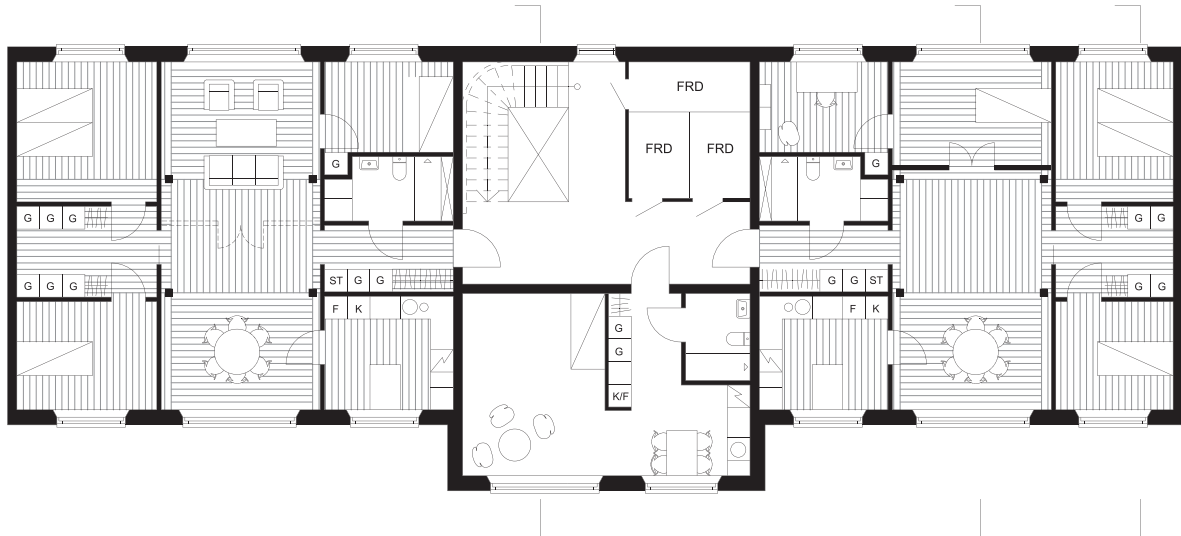

Plan 1-4, princip alt. 1 —Bostäder

Bostadsplan

Bostaden har ett centralt rum, som går från fasad-till-fasad i lägenheten. Från detta rum nås övriga rum. Det centrala rummet kan antingen lämnas öppet, eller delas av i flera rum och kan på så sätt möjliggöra flera olika användningar och situationer. Två av sovrummen har entré från en gemensam klädkammare, vilket ger avskildhet och möjlighet till ostörd vila. Lägenheten har en mer publik sida mot gatan med kök och matplats.

Konstruktion


Byggnadens konstruktion består av en bärande vägg med en yttre mur av fasadtegel och en inre mur av tegelmurblock. Detta ger en vägg som främst består av tegel, men som är snabbare och billigare att producera på grund av tegelmurblockens större format. Den inre konstruktionen består av pelare och balkar i limträ, på vilken vilar en platsgjuten betongskiva.


Generalitet & Flexibilitet

Eftersom bärningen ligger i fasaden och pelar/balkkonstruktionen är den inre planen fri att utformas på olika vis för att kunna skapa olika bostadsplaner eller helt byta användningsområde till för exempel kontor, butikslokal, eller annan verksamhet. Schakt är samlade mot trapphuset vilket lämnar den inre ytan fri.


Entréplanet har ökad föränderlighet inbyggd i fasaden. Ytan under fönsten är murad separat från resterande vägg, vilket ger möjlighet att anpassa fönster och addera dörrar beroende på användning.

Mellanjälklaget är utformat för att kunna öppnas upp över flera våningar, för att till exempel kunna skapa större kontor.

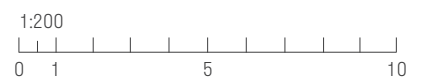

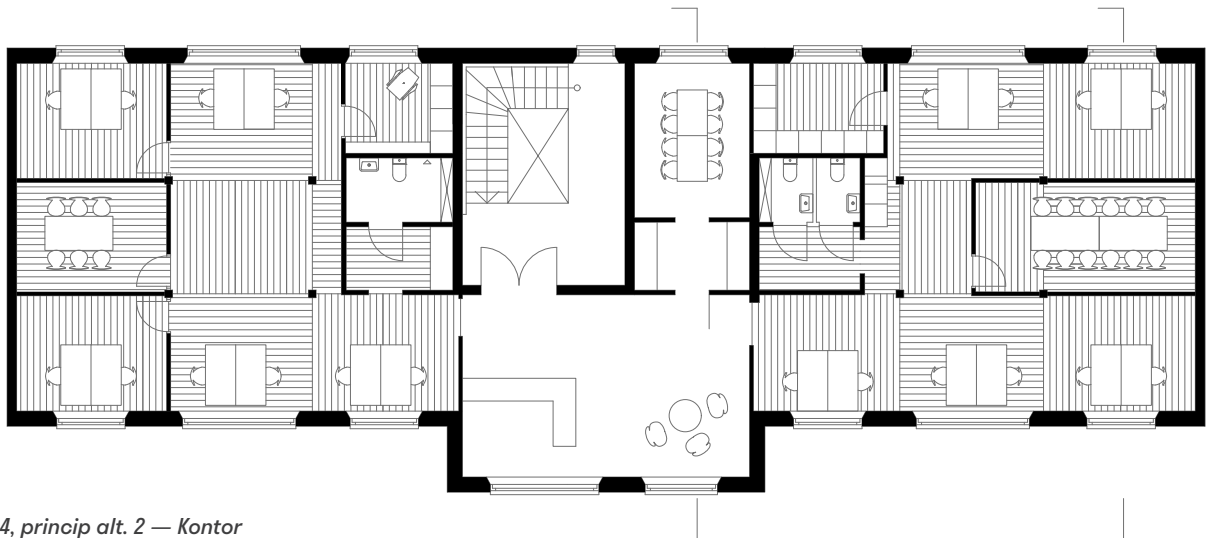

Plan 1-4, princip alt. 2 — Kontor

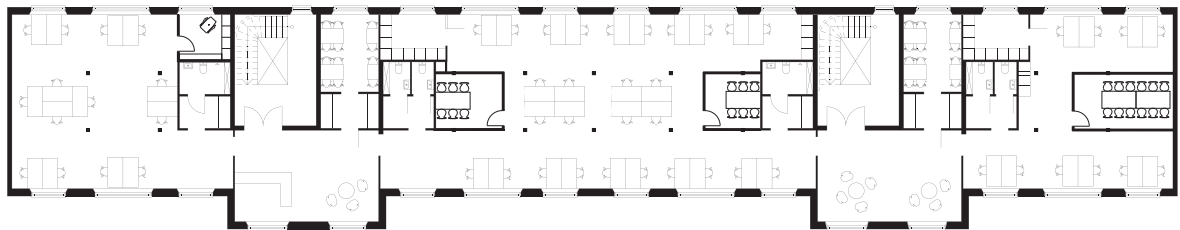

Plan 1-4, princip — Storkontor

skala 1:200

Kontor

Den flexibla konstruktionen tillåter flera användningar, här som kontor. Planen tillåter användning som kontorslandskap, samt uppdelning i mötesrum och cellkontor. Vid behov kan kontor sammanlänkas genom flera hus. Eftersom konstruktionen är gjord på pelare kan öppningar för trappor mellan våningar enklare för att ha intern kommunikation mellan våningar.

Fasad







Fasad, skala 1:200

Fasaden är i rött tegel, ett material som återkommer i befintlig bebyggelse i närområdet. Materialet tegel åldras vackert och kräver litet underhåll.

Fönster och våningar markeras med en något utskjutande sten, vilket både ger skuggverkan och liv till fasaden samt berättar om byggnadens insida.

Fasaden har en enkel rytm. Vartannat fönster är något mindre (sovrums- och köksfönster), medan större fönster markerar vardagsrum.

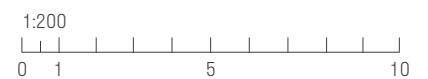

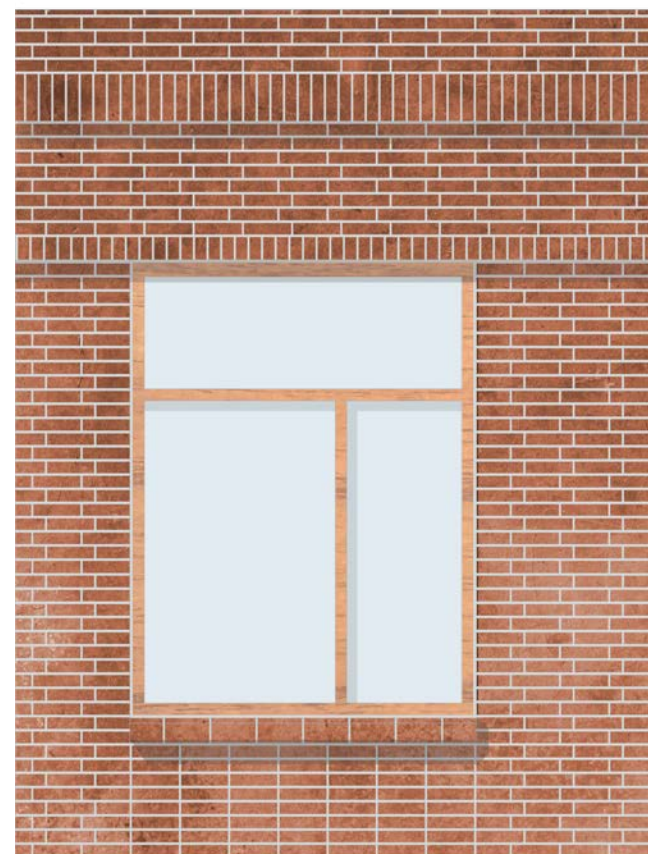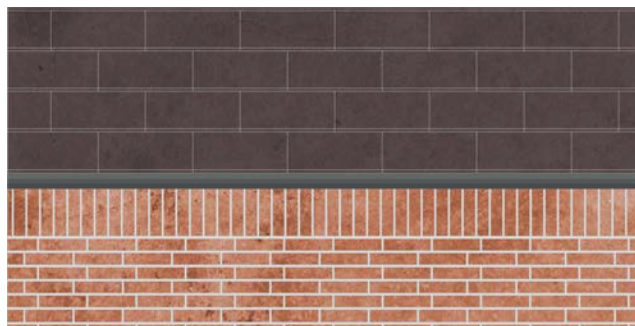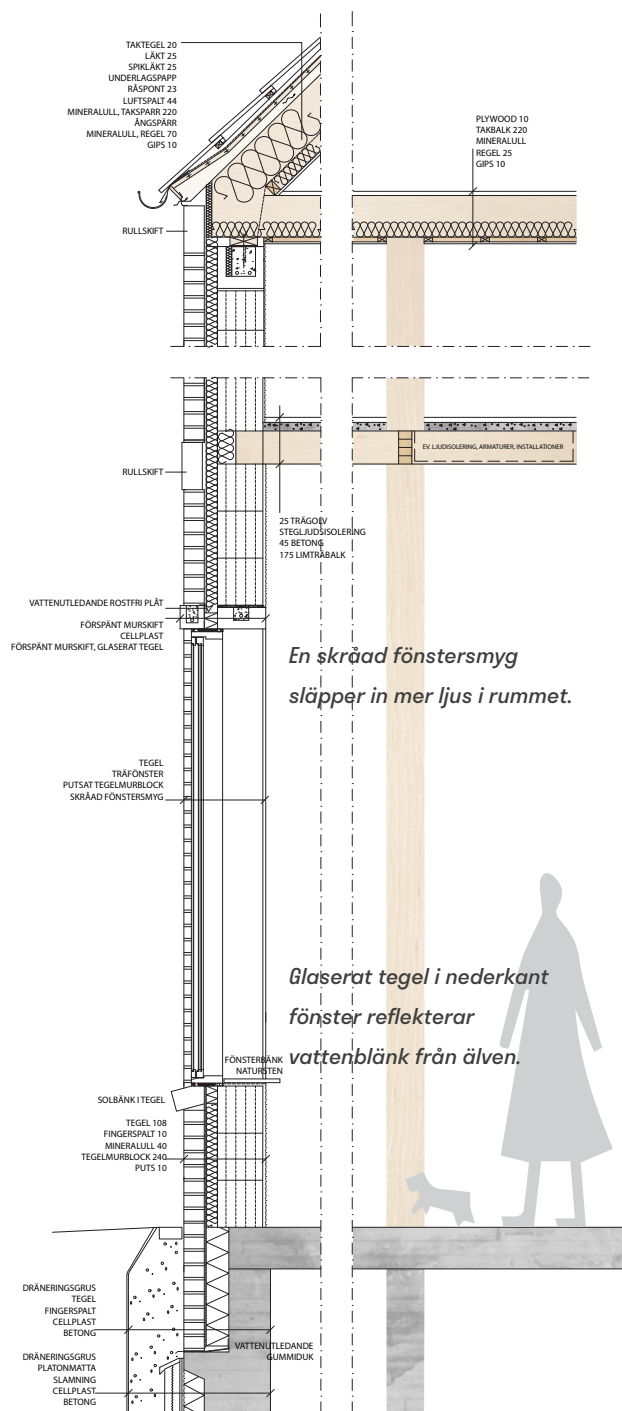

*Tegelstenar under fönster
lätta att ta bort för att
kunna ersätta med fönster
med lägre bröstning, eller
dörrar.*

*Skift som kragar ut ger
skuggverkan, markerar
våningar och fönster.*

FASADSEKTION & FASADUTSNITT

SKALA 1:40

